


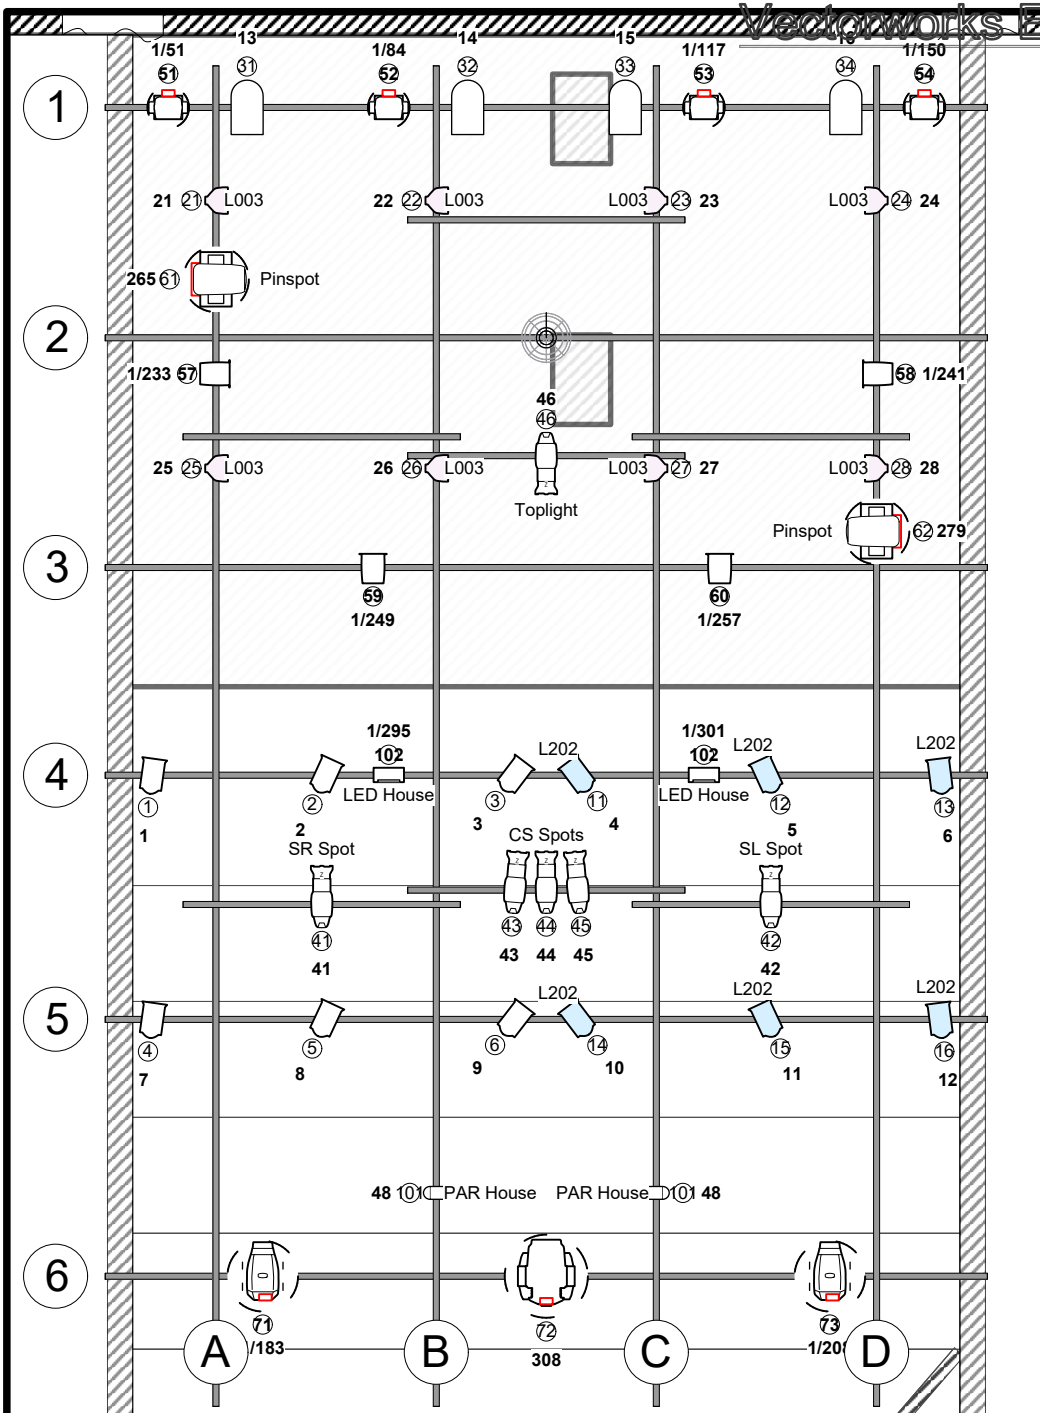

	Selecon Acclaim Fresnel	12
	PAR64 CP62 MFL	4
	ETC S4 PAR MFL	8
	ETC S4 Jr Zoom	6
	Prolights StudioCOB FC 150	4
	Chauvet Rogue R2X Wash	4
	Chauvet Intimidator Spot LED 350	2
	BeamZ Ignite400	2
	Martin MAC TW1	1
	Stairville Wild Wash 132	2
	PAR38 FL	2

Color	Size	Count
L202	125mm	6
L003	190mm	8

1

Rig Plan

Scale: 1:60

Typical Generic

Purpose
Color
Gobo 1
Dimmer
Channel
Absolute Address

Typical Intelligent

Purpose
Channel
Universe/Address

Show Name

Bedlam Fringe 2025

Title

Rig Plan

Drawn By

Leon Lee



Date

23/07/2025

Venue

Bedlam Theatre

APPLEBY
TECHNICAL

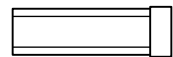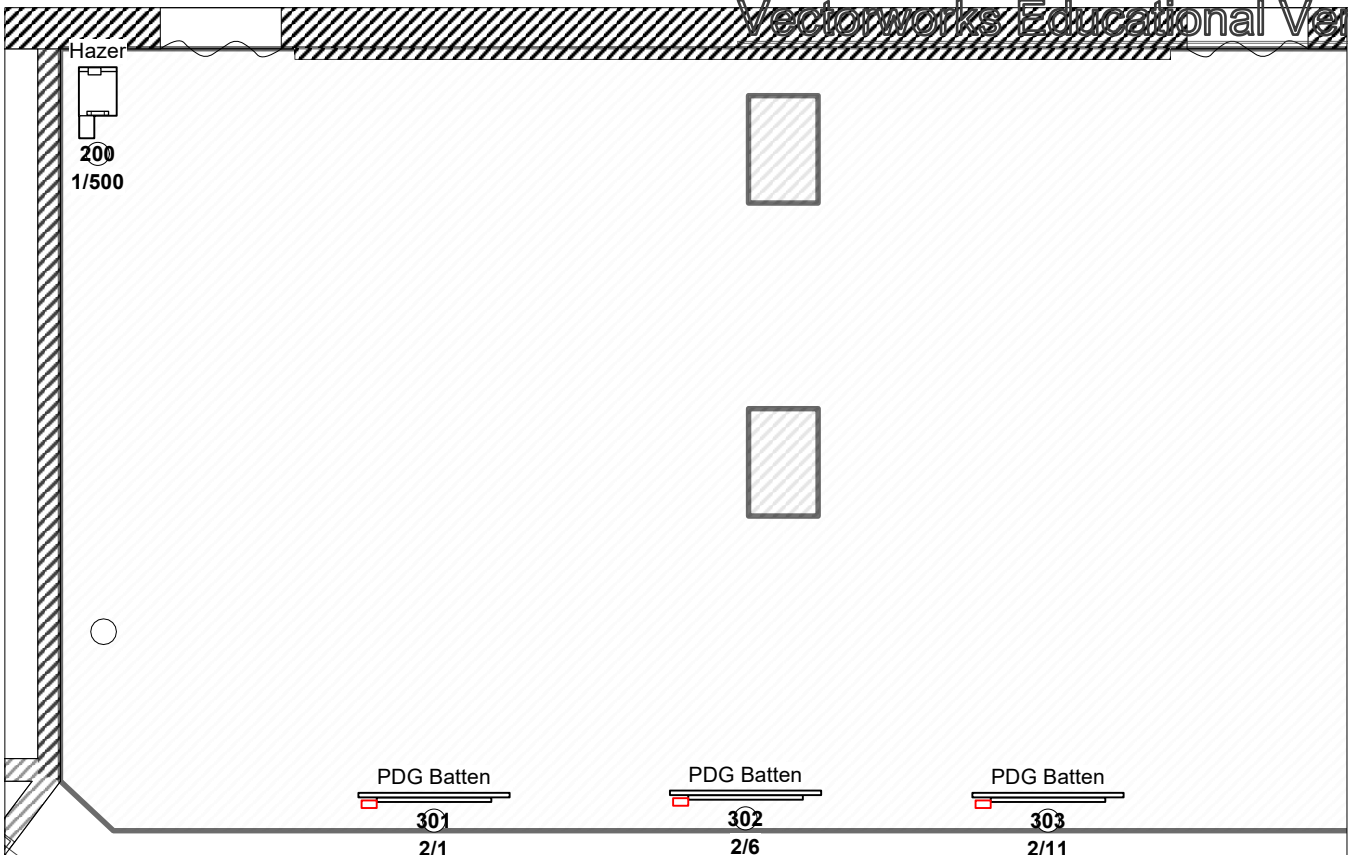


Selecon Chorus Followspot 1





Look Solutions Unique 2.1 1



Stairville Show Bar TriLED 18x3W RGB 3

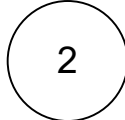

Hazer
Scale: 1:50

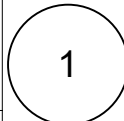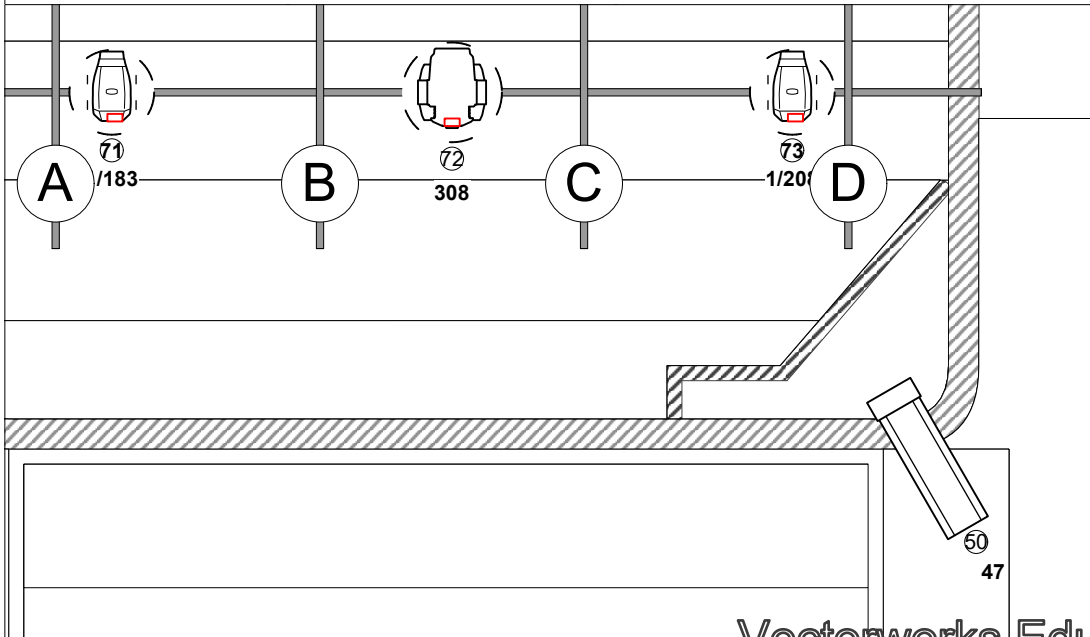

Followspot
Scale: 1:50

Typical Generic

Typical Intelligent

Purpose
Color
Gobo 1
Dimmer
Channel
Absolute Address

Purpose
Channel
Universe/Address

Show Name Bedlam Fringe 2025		
Title Rig Plan Other	Drawn By Leon Lee	Date 23/07/2025
Venue Bedlam Theatre		APPLEBY TECHNICAL