


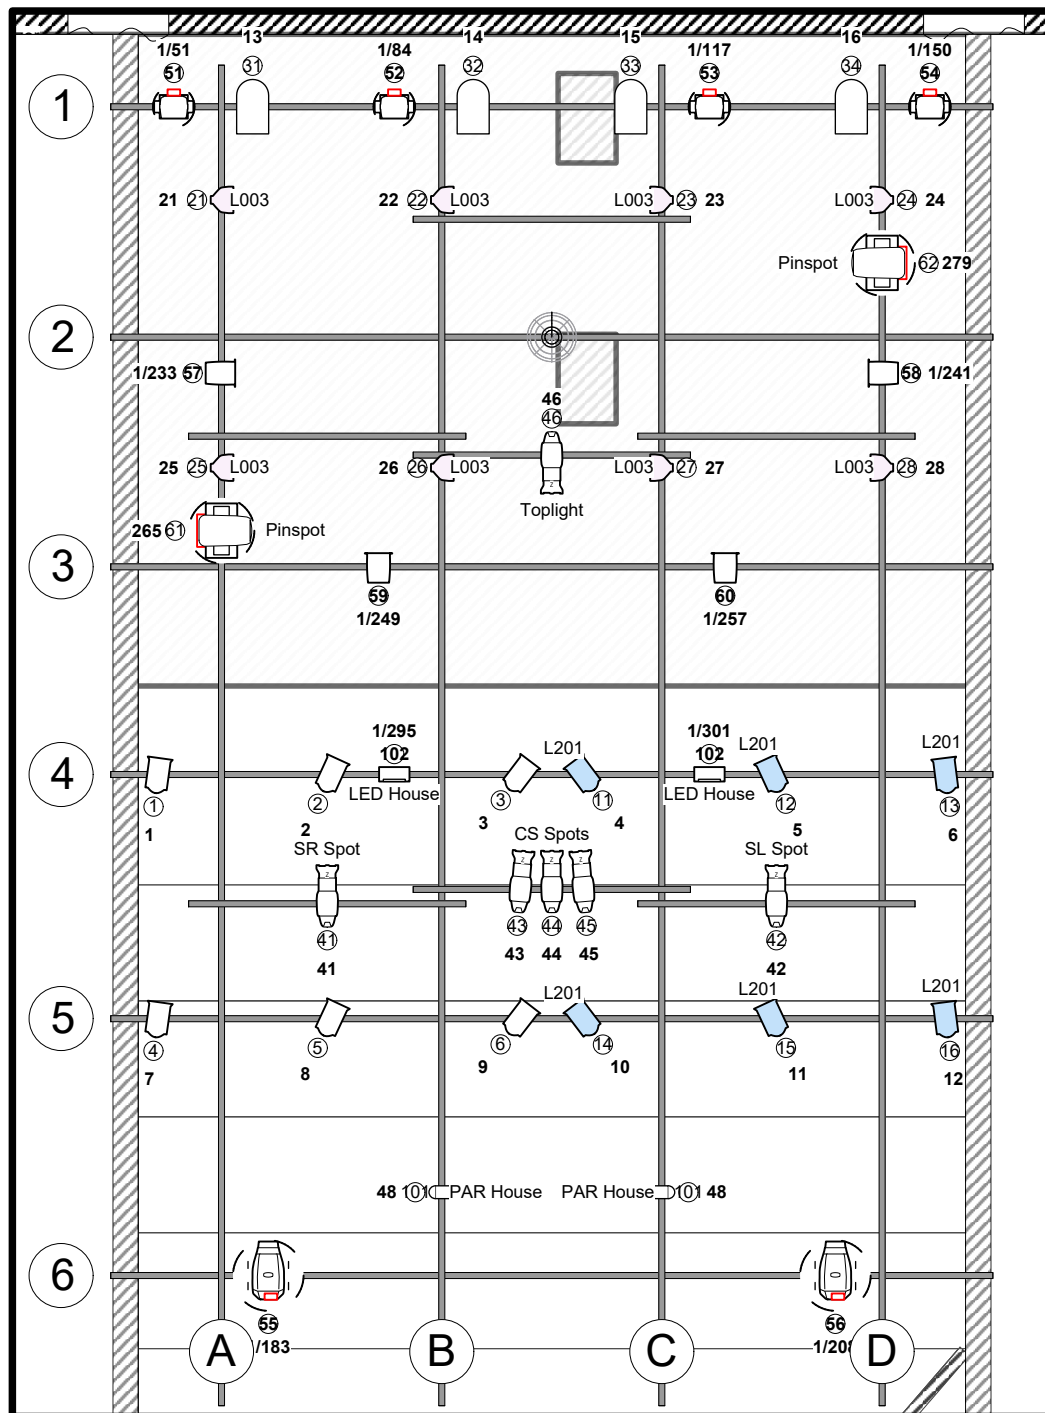

Selecon Acclaim Fresnel

12



PAR64 CP62 MFL

4



ETC S4 PAR MFL

8



ETC S4 Jr Zoom

3



Prolights StudioCOB FC 150

4



Chauvet Rogue R2X Wash

4



Chauvet Intimidator Spot LED 350

2



BeamZ Ignite400

2



Stairville Wild Wash 132

2



PAR38 FL

2

Color	Size	Count
● L201	125mm	6
● L003	190mm	8

1

Rig Plan

Scale: 1:60

Typical Generic

Purpose
Color
Gobo 1
Dimmer
Channel
Absolute Address

Typical Intelligent

Purpose
Channel
Universe/Address

Show Name

Bedlam Fringe 2025

Title

Rig Plan

Drawn By


Leon Lee

Date


28/06/2025

Venue


Bedlam Theatre - Sponsored by Appleby Technical

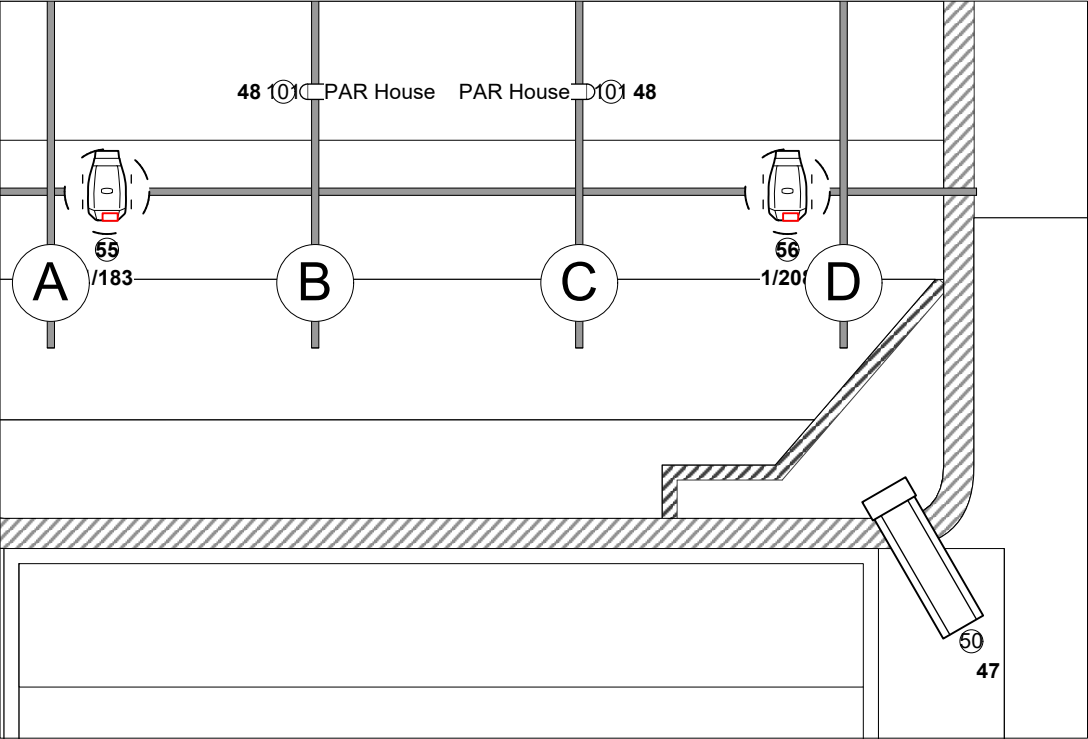

1 Followspot
Scale: 1:50

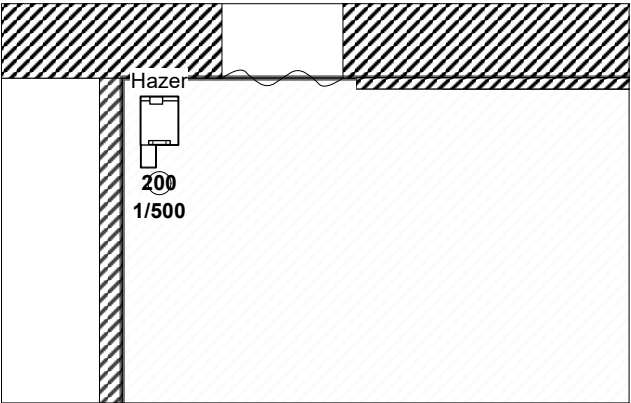

2 Hazer
Scale: 1:50

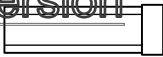

Selecon Chorus Followspot

1



Look Solutions Unique 2.1

1

Typical Generic

Purpose
Color
Gobo 1
Dinner
Channel
Absolute Address

Typical Intelligent

Purpose
Channel
Universe/Address

Show Name

Bedlam Fringe 2025

Title

Rig Plan Other

Drawn By


Leon Lee

Date

28/06/2025

Venue

Bedlam Theatre - Sponsored by Appleby Technical

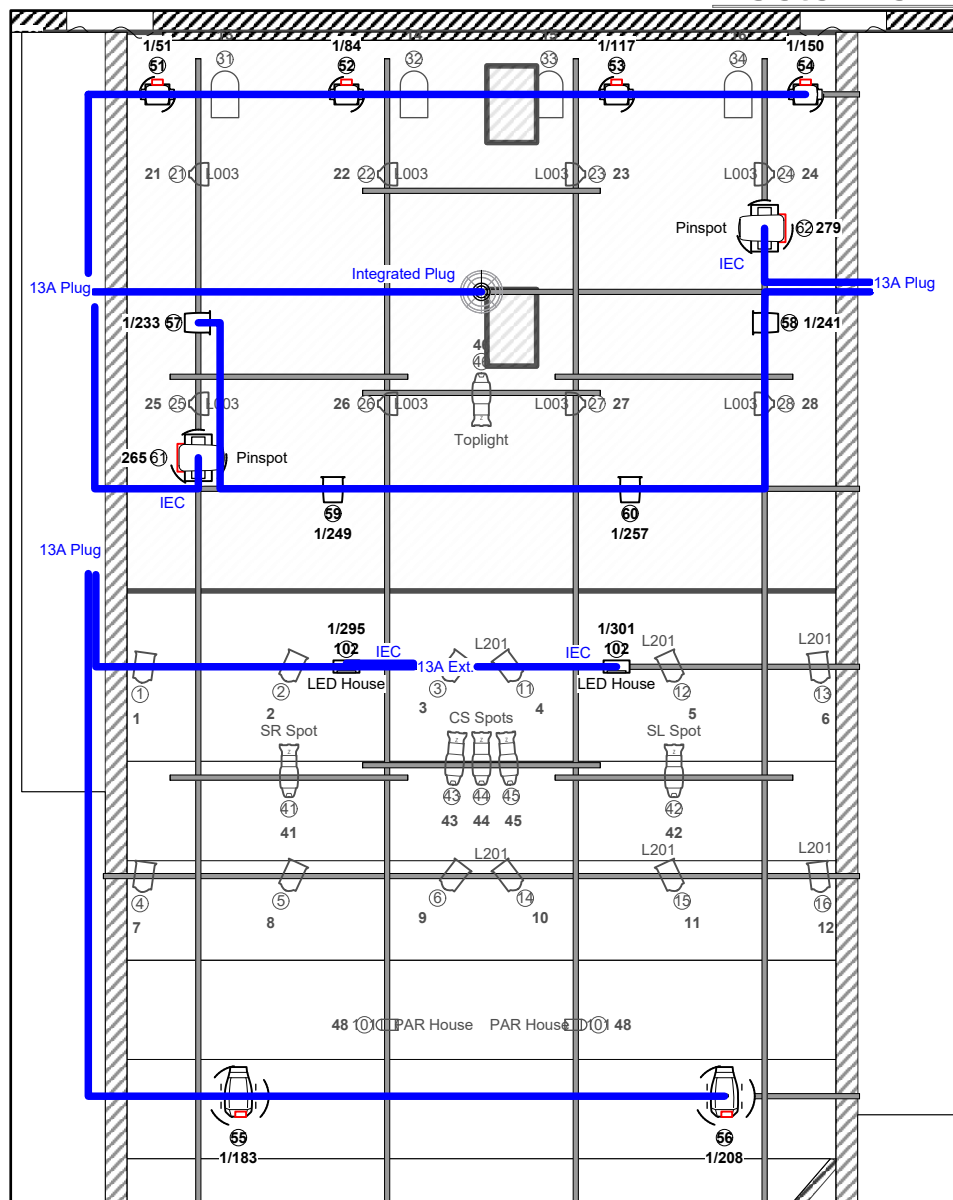

1


Power Plan

Scale: 1:70

2

DMX Plan

Scale: 1:70

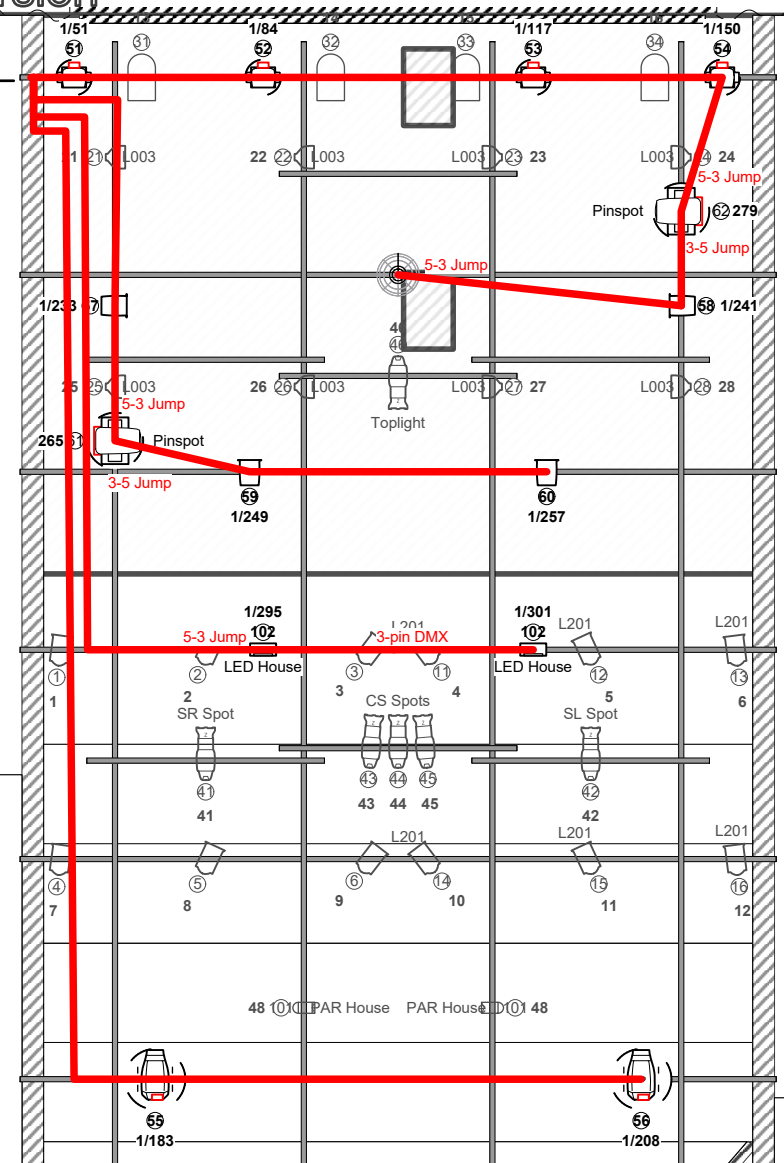

Show Name

Bedlam Fringe 2025

Title	Author	Year	Source

Cable Plan

Drawn By	
----------	--

Leon Lee

Date

21/07/2025

Venue,

Venue
Bedlam Theatre - Sponsored by Appleby Technical