


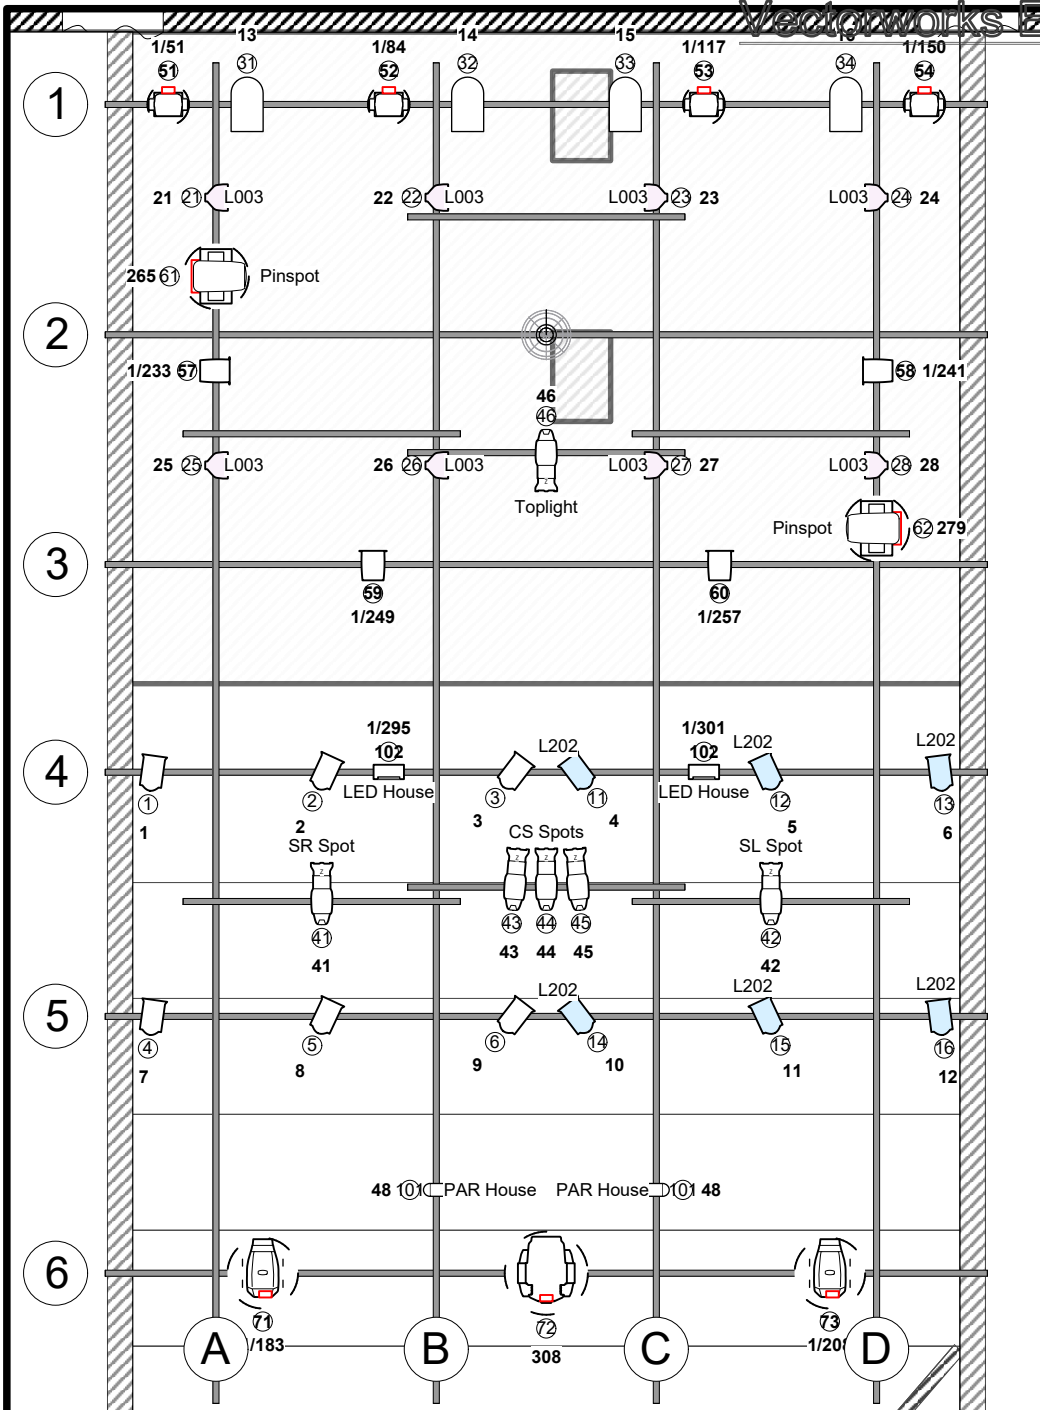

	Selecon Acclaim Fresnel	12
	PAR64 CP62 MFL	4
	ETC S4 PAR MFL	8
	ETC S4 Jr Zoom	6
	Prolights StudioCOB FC 150	4
	Chauvet Rogue R2X Wash	4
	Chauvet Intimidator Spot LED 350	2
	BeamZ Ignite400	2
	Martin MAC TW1	1
	Stairville Wild Wash 132	2

Color	Size	Count
	L202	125mm 6
	L003	190mm 8

1

Rig Plan

Scale: 1:60

Typical Generic

Purpose
Color
Gobo 1
Dimmer
Channel
Absolute Address


Typical Intelligent

Purpose
Channel
Universe/Address


Show Name


Bedlam Fringe 2025

Title
Rig PlanDrawn By
Leon LeeDate
29/07/2025Venue
Bedlam TheatreAPPLEBY
TECHNICAL

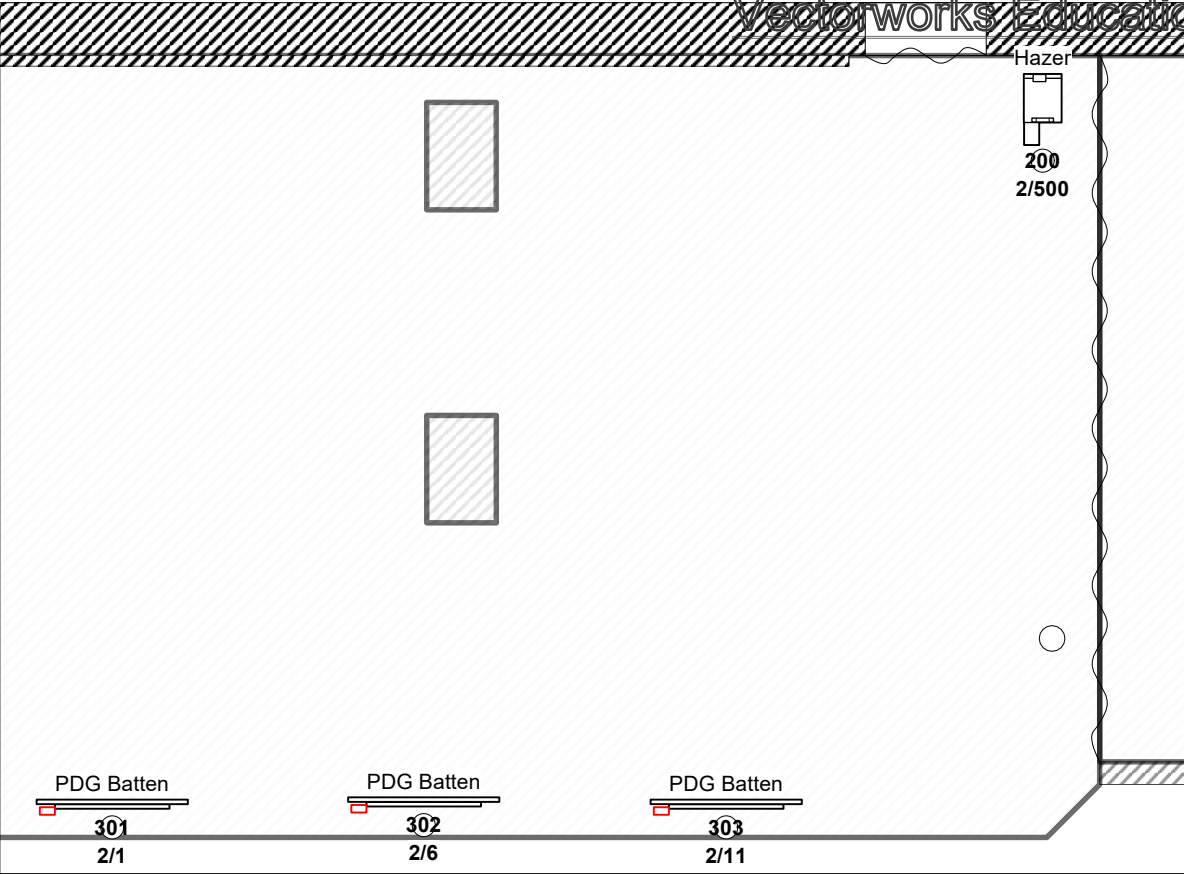

2 Hazer
Scale: 1:50

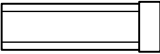	Selecon Chorus Followspot	1
	Look Solutions Unique 2.1	1
	Stairville Show Bar TriLED 18x3W RGB	3

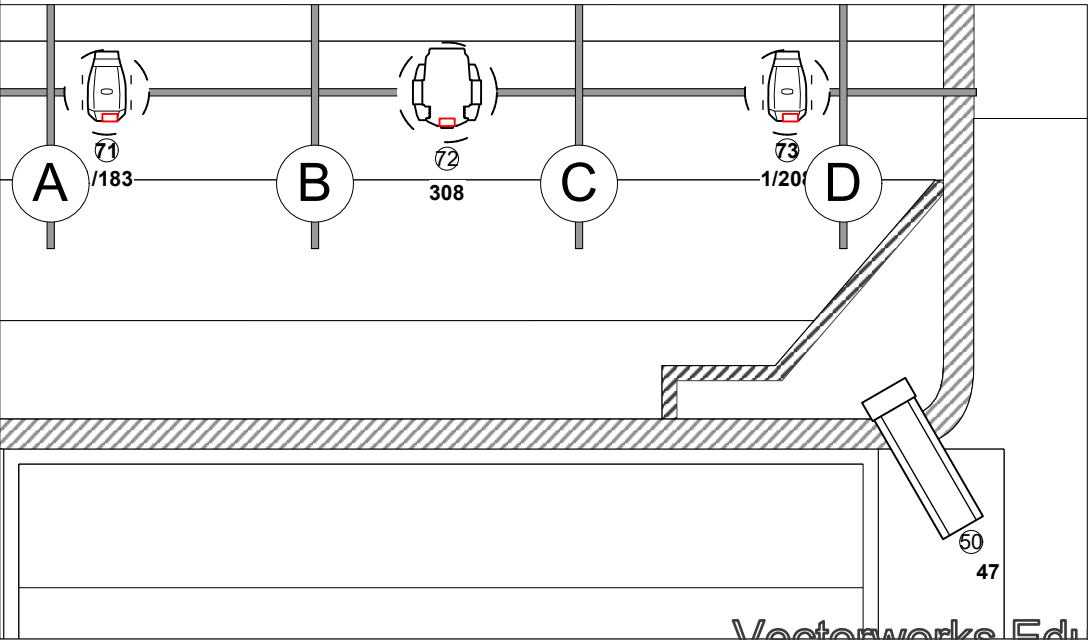

1 Followspot
Scale: 1:50

Typical Generic	Typical Intelligent
Purpose	Purpose
Color	Color
Gobo 1	Channel
Dimmer	Channel
Channel	Channel
Absolute Address	Universe/Address

Show Name Bedlam Fringe 2025		
Title Rig Plan Other	Drawn By Leon Lee	Date 29/07/2025
Venue Bedlam Theatre		APPLEBY TECHNICAL